
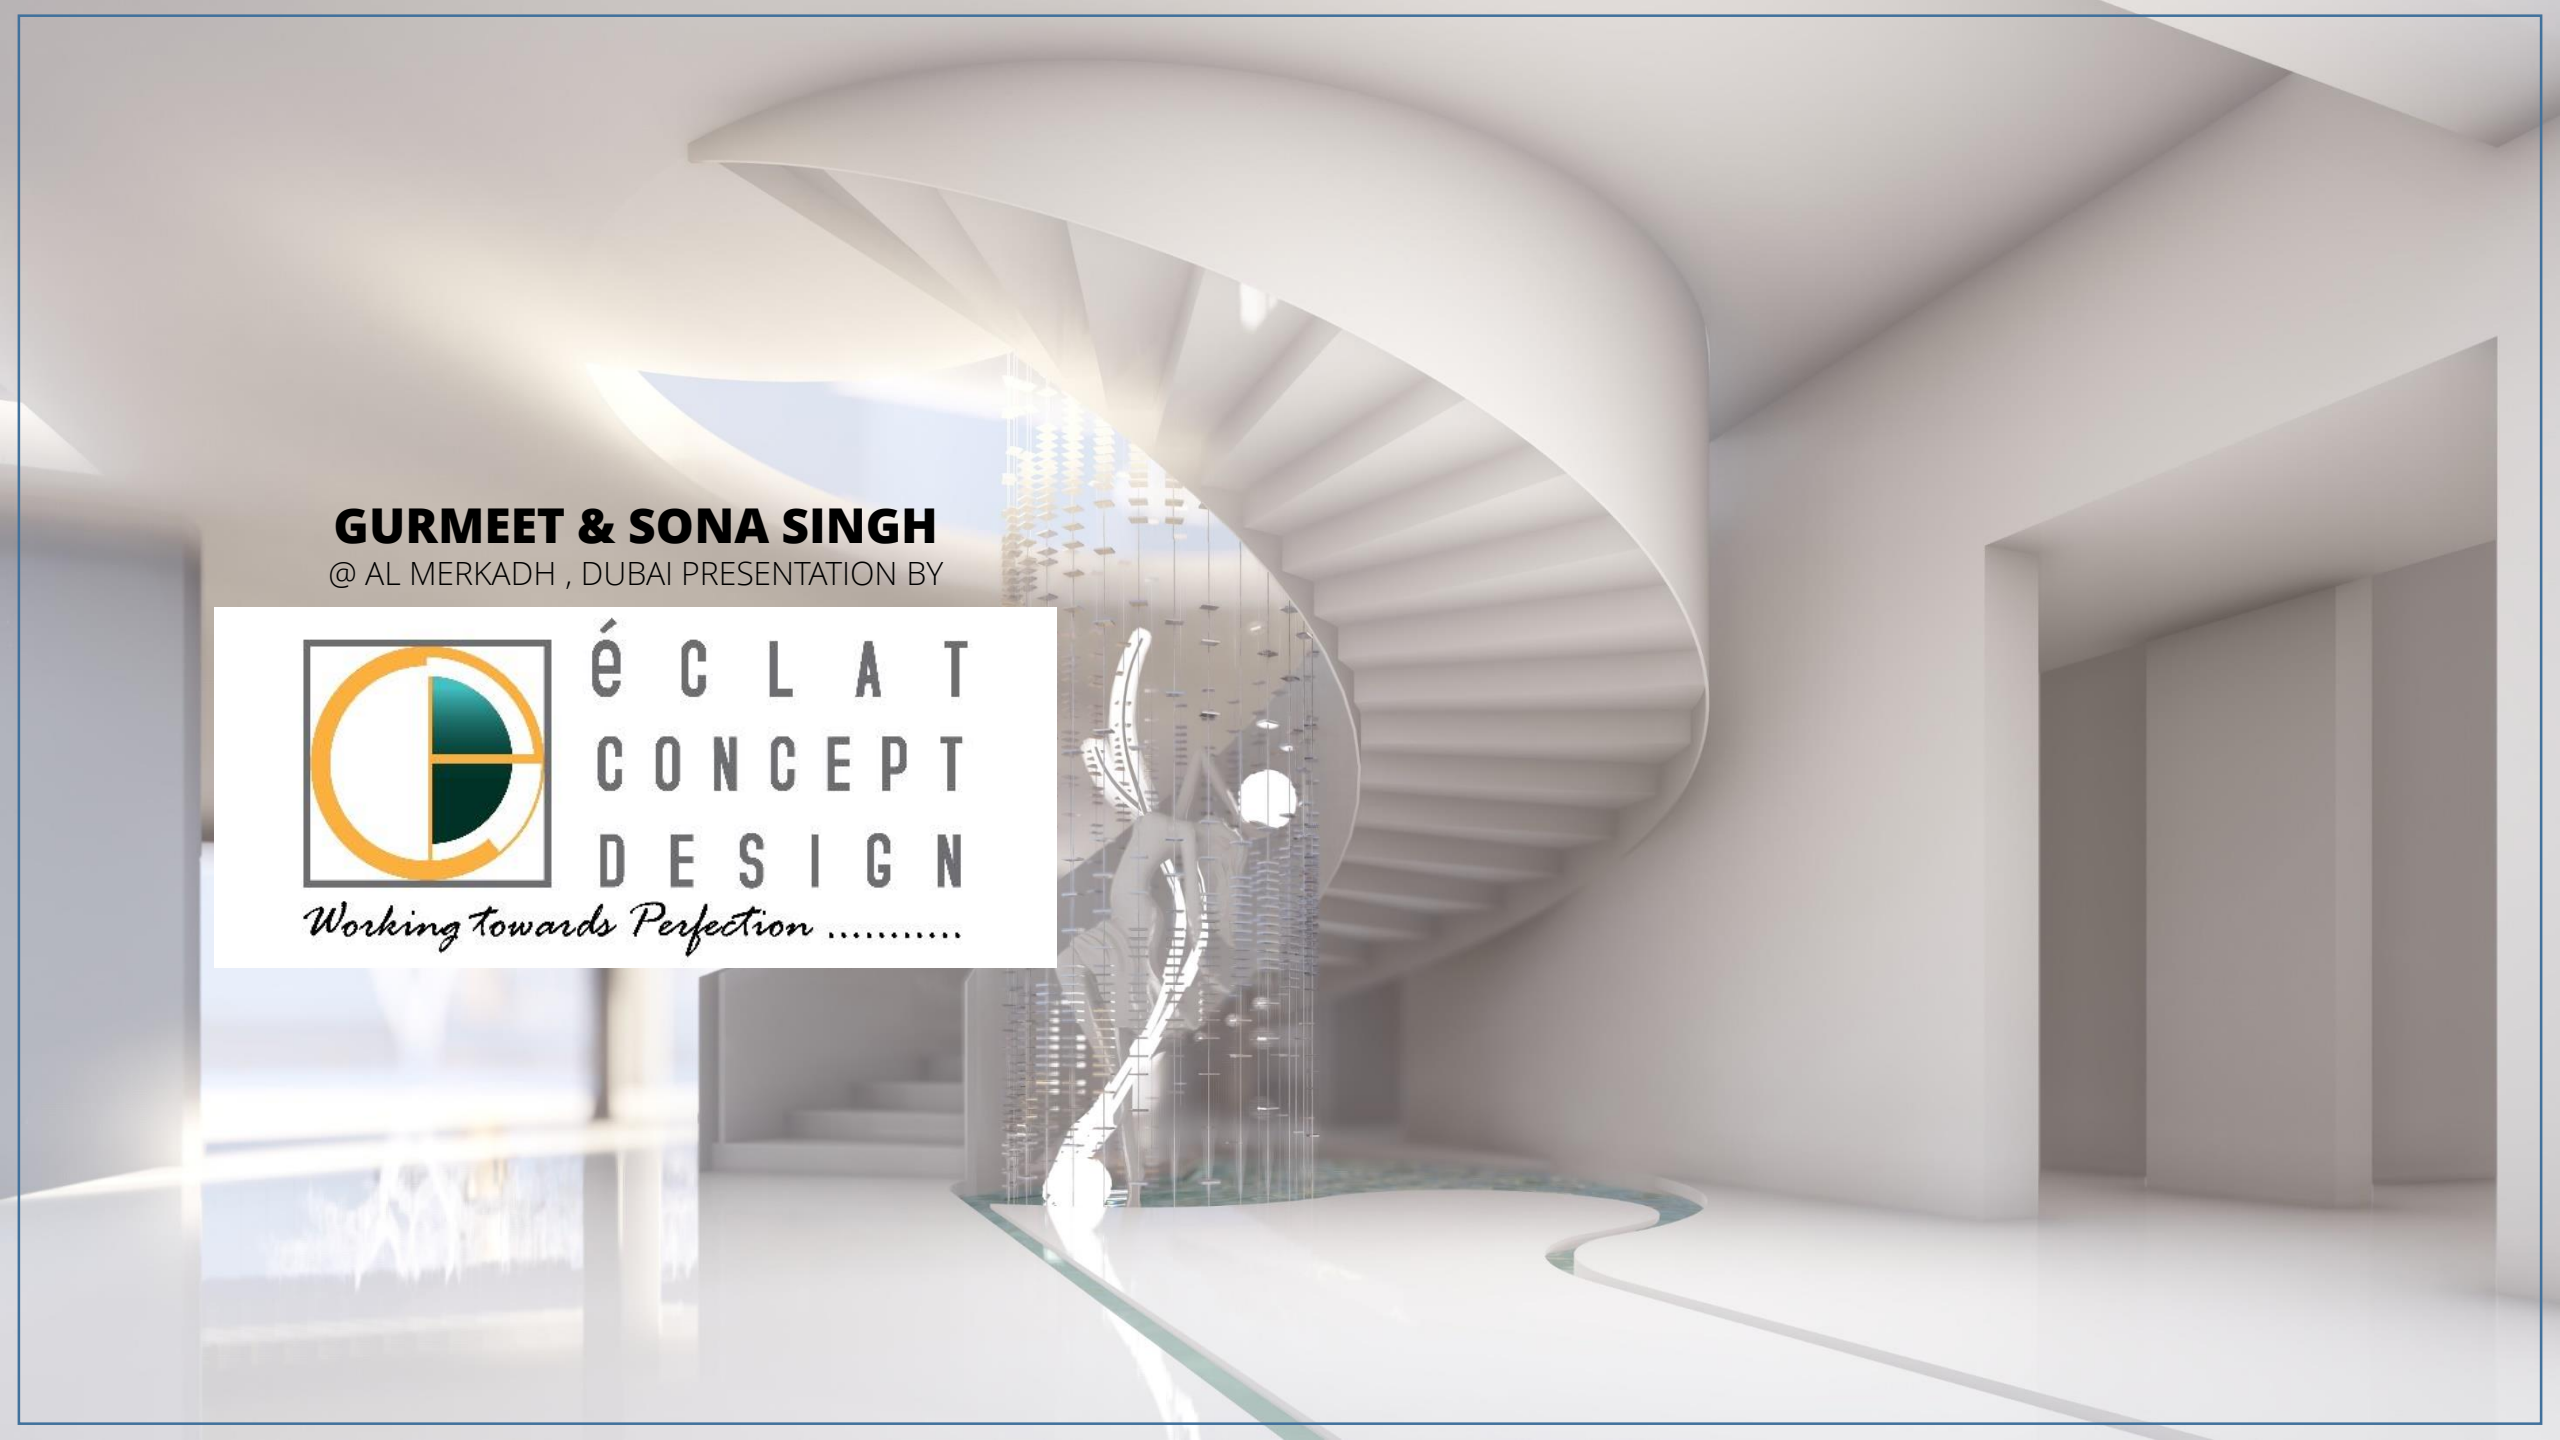


GURMEET & SONA SINGH

@ AL MERKADH , DUBAI PRESENTATION BY

éCLAT CONCEPT DESIGN

Working towards Perfection .....

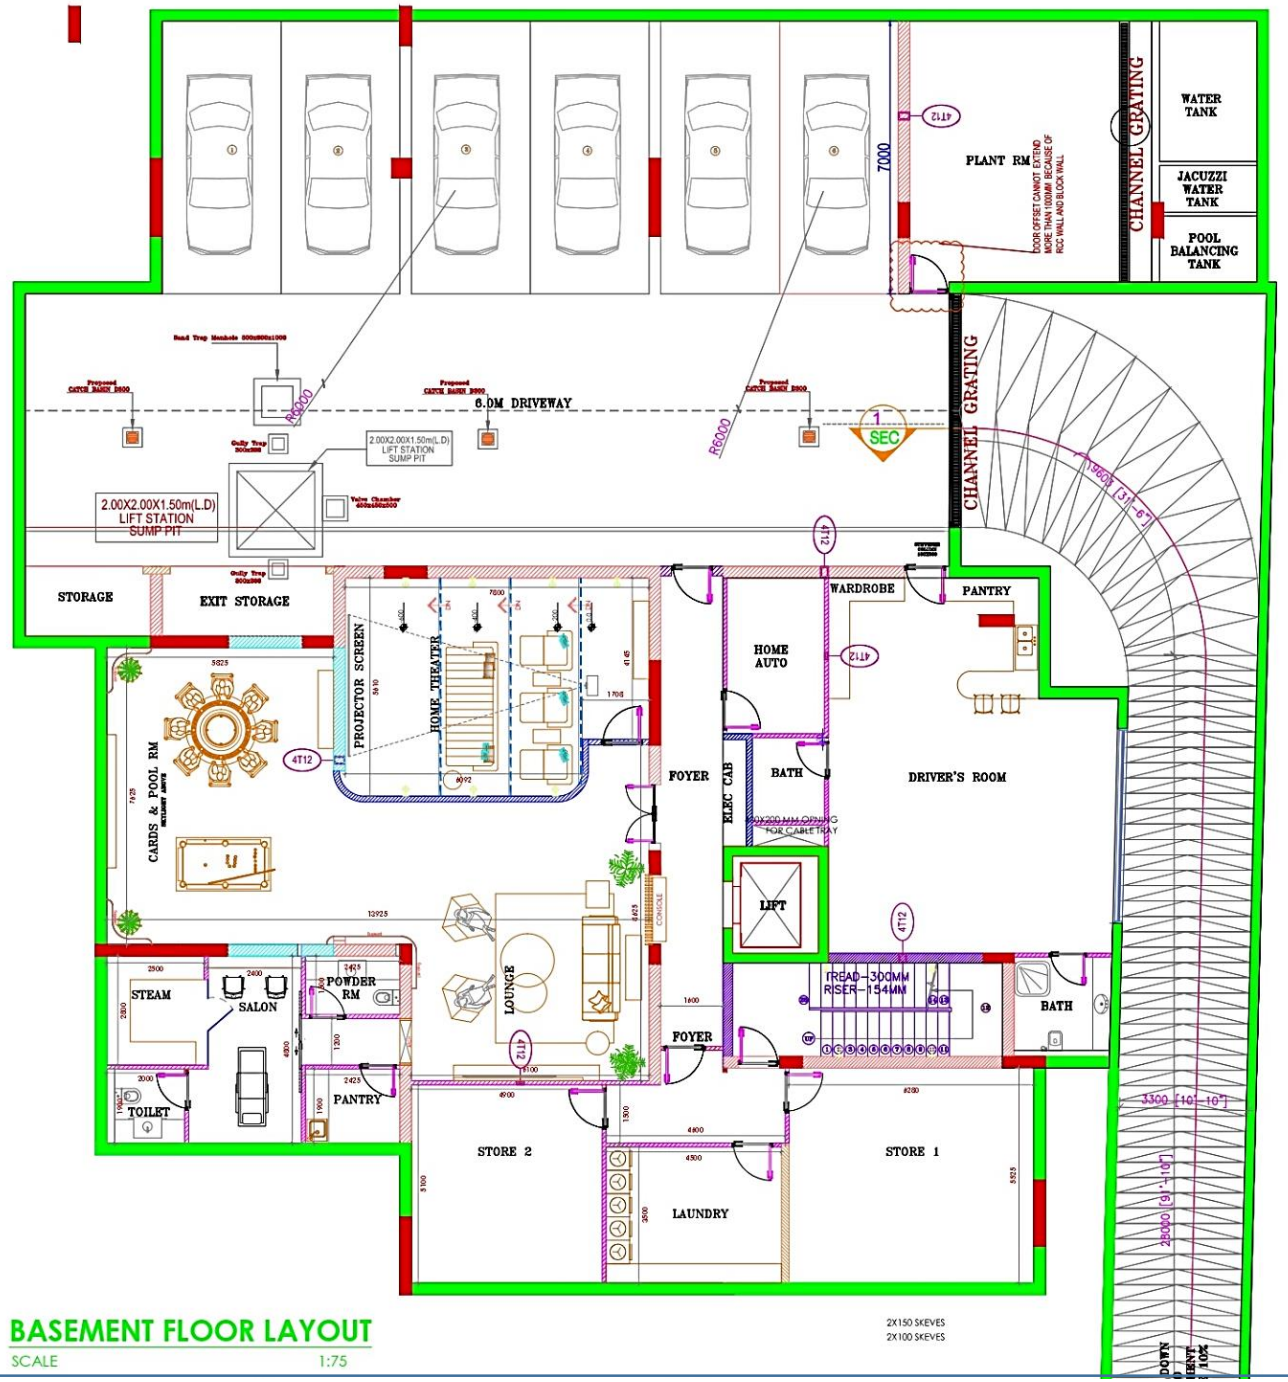

BASEMENT FLOOR LAYOUT

SCALE 1:75

BASEMENT LAYOUT

éCLAT CONCEPT DESIGN

Working towards Perfection .....



BASEMENT FLOOR-ENTRANCE LOUNGE

éCLAT CONCEPT DESIGN
Working towards Perfection .....



BASEMENT FLOOR-VIEW FROM LOUNGE TO PLAY AREA

éCLAT CONCEPT DESIGN
Working towards Perfection .....



BASEMENT FLOOR PLAY AREA

éCLAT CONCEPT DESIGN
Working towards Perfection .....



BASEMENT FLOOR - HOME THEATER SITTING VIEW

éCLAT CONCEPT DESIGN
Working towards Perfection .....



BASEMENT FLOOR - HOME THEATER SCREEN VIEW

éCLAT CONCEPT DESIGN
Working towards Perfection .....



GROUND FLOOR LAYOUT

éCLAT CONCEPT DESIGN

Working towards Perfection .....



GROUND FLOOR LAYOUT

éCLAT CONCEPT DESIGN

Working towards Perfection .....



MAIN ENTRANCE WALL FEATURE

éCLAT CONCEPT DESIGN

Working towards Perfection .....



LOBBY


éCLAT CONCEPT DESIGN

Working towards Perfection .....



LOBBY

éCLAT CONCEPT DESIGN
Working towards Perfection .....

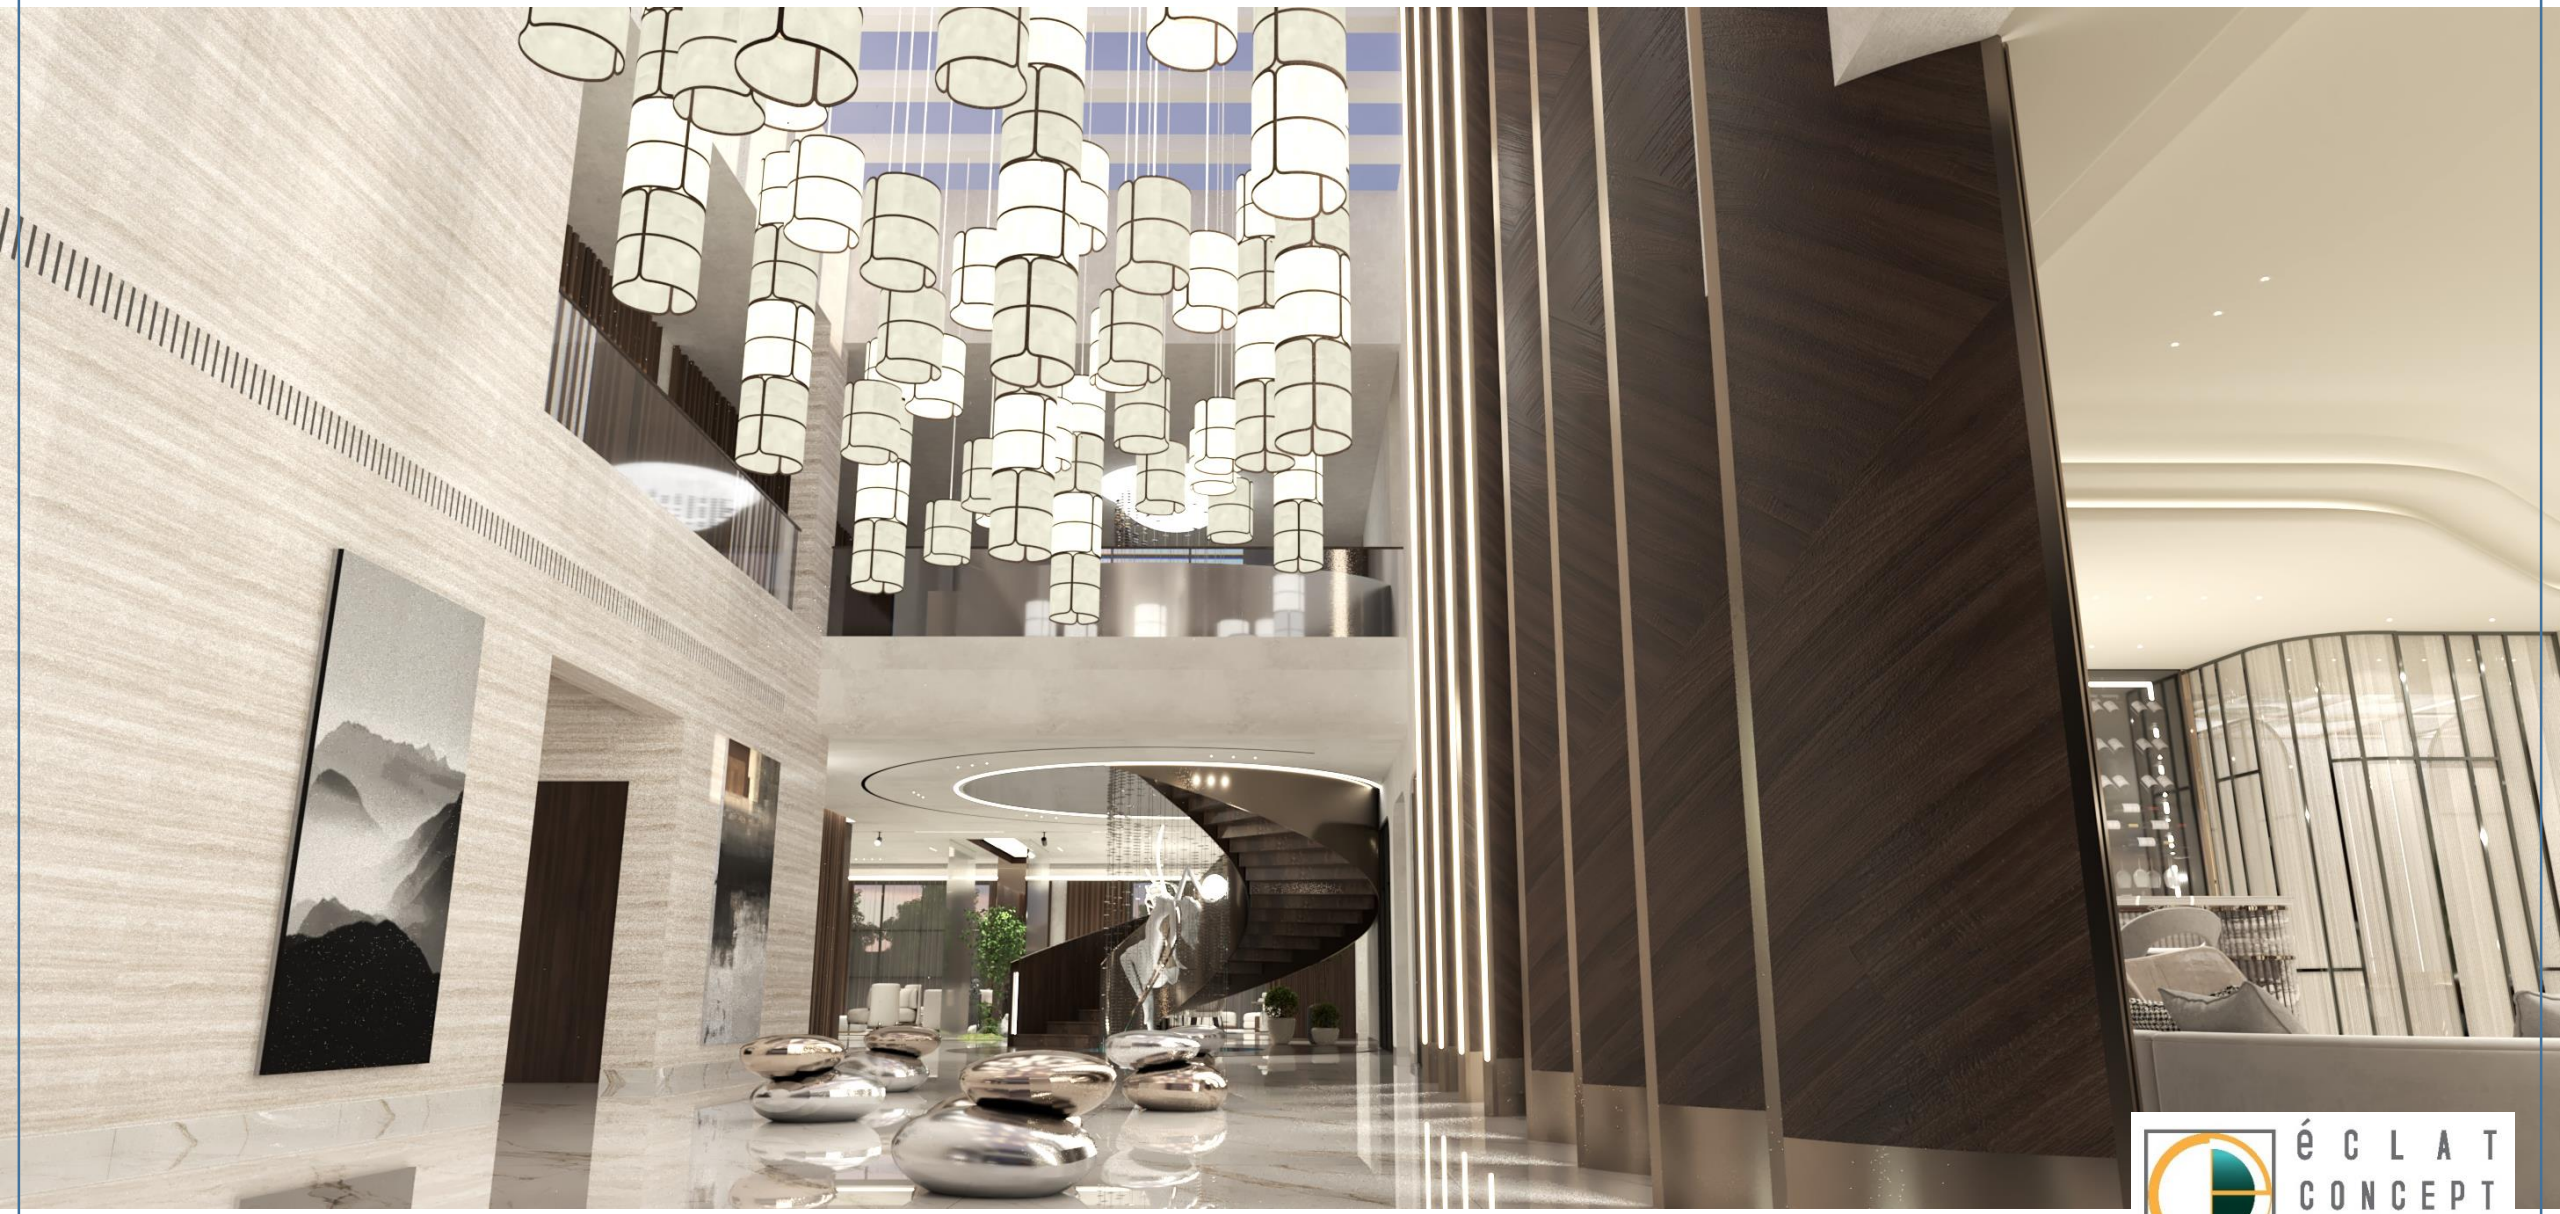

LOBBY

éCLAT CONCEPT DESIGN
Working towards Perfection .....



LOBBY

éCLAT CONCEPT DESIGN

Working towards Perfection .....



FORMAL LIVING

éCLAT CONCEPT DESIGN

Working towards Perfection .....




FORMAL LIVING

éCLAT CONCEPT DESIGN

Working towards Perfection .....



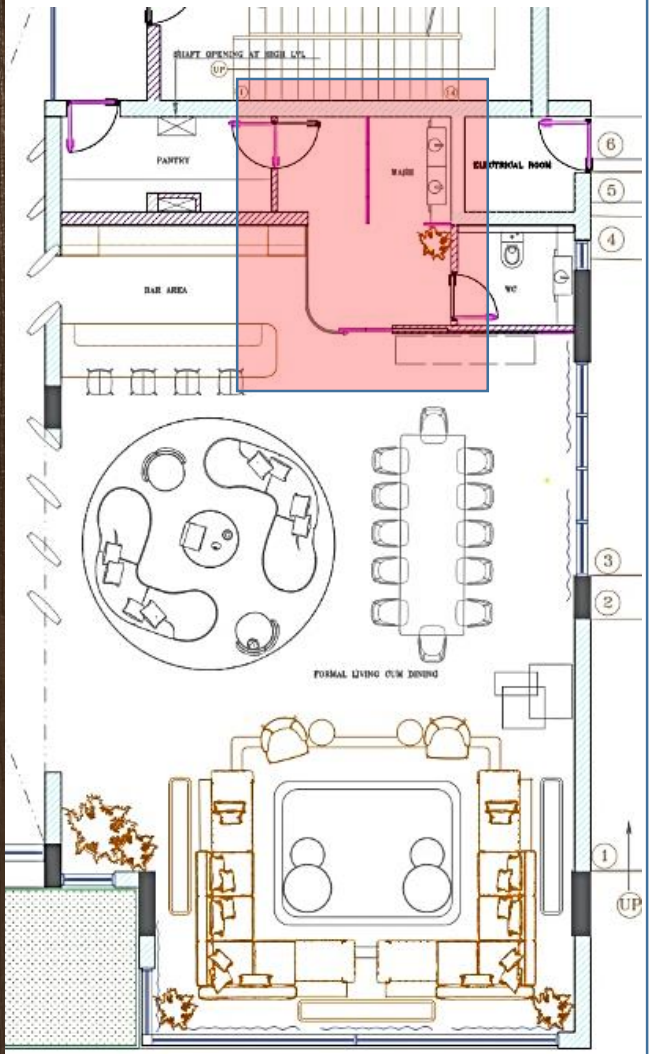

WASH

éCLAT CONCEPT DESIGN

Working towards Perfection .....



STAIRCASE

éCLAT CONCEPT DESIGN

Working towards Perfection .....



STAIRCASE

éCLAT CONCEPT DESIGN

Working towards Perfection .....



FAMILY LIVING

éCLAT CONCEPT DESIGN

Working towards Perfection .....



FAMILY LIVING

éCLAT CONCEPT DESIGN

Working towards Perfection .....



FAMILY LIVING


éCLAT CONCEPT DESIGN

Working towards Perfection .....



POOJA ROOM


éCLAT CONCEPT DESIGN
Working towards Perfection .....

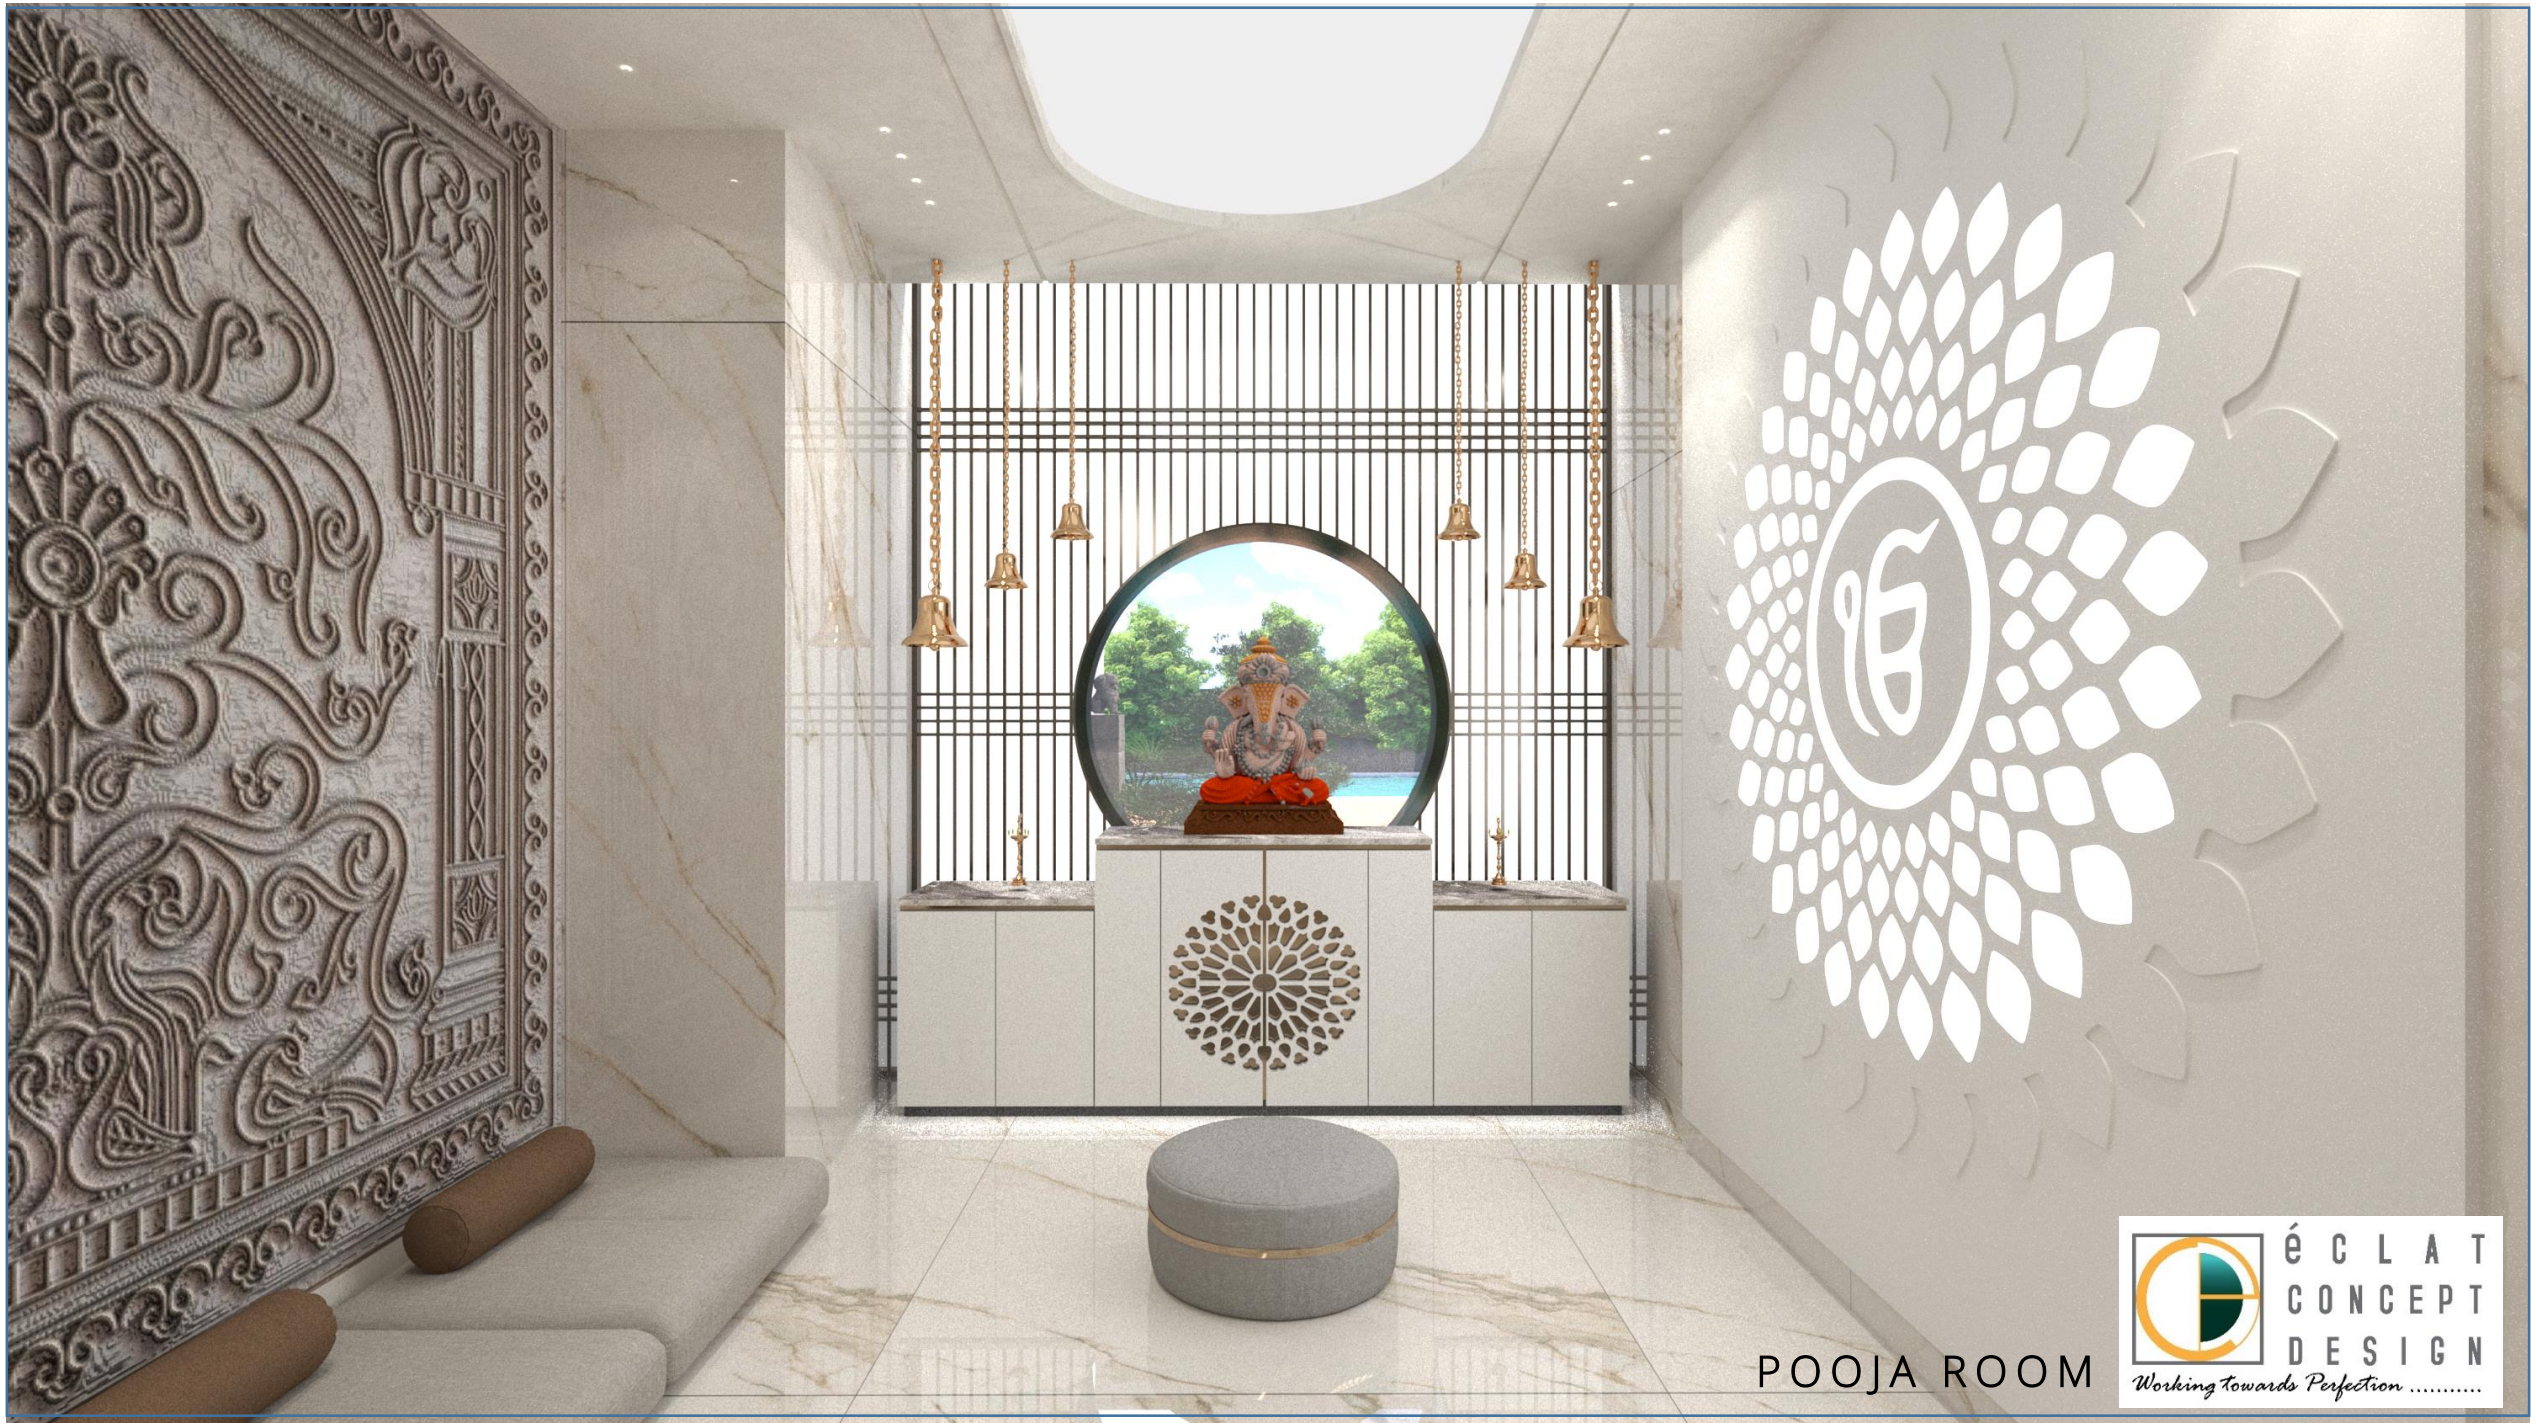

POOJA ROOM

éCLAT CONCEPT DESIGN
Working towards Perfection .....



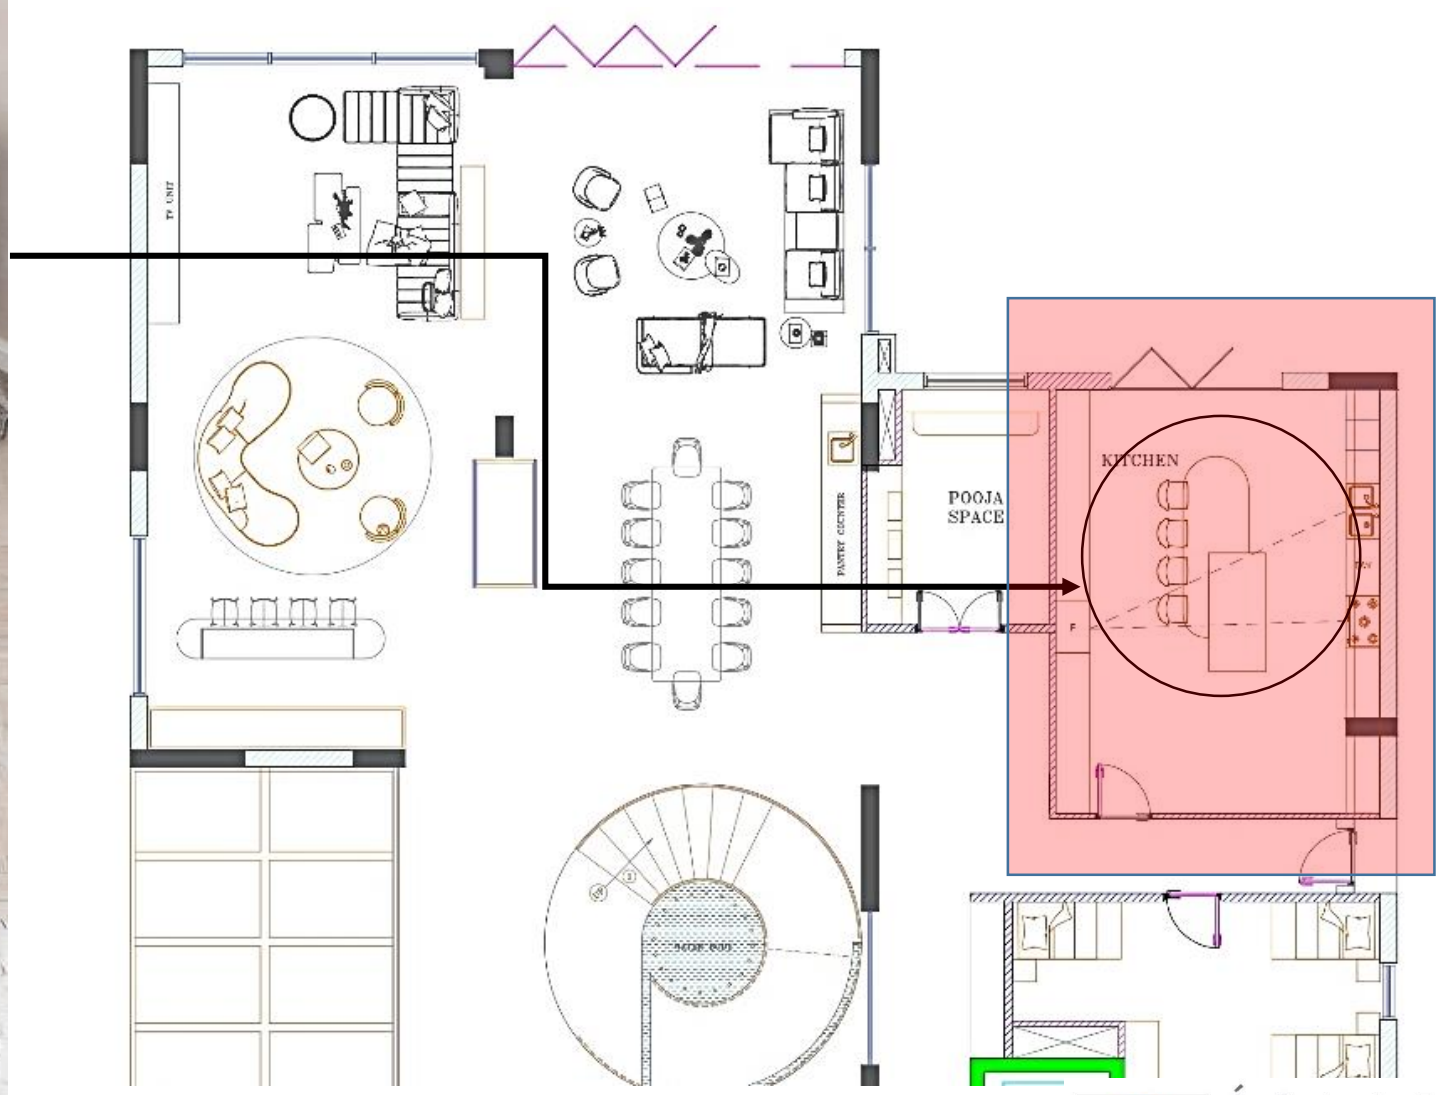


KITCHEN

éCLAT CONCEPT DESIGN

Working towards Perfection .....



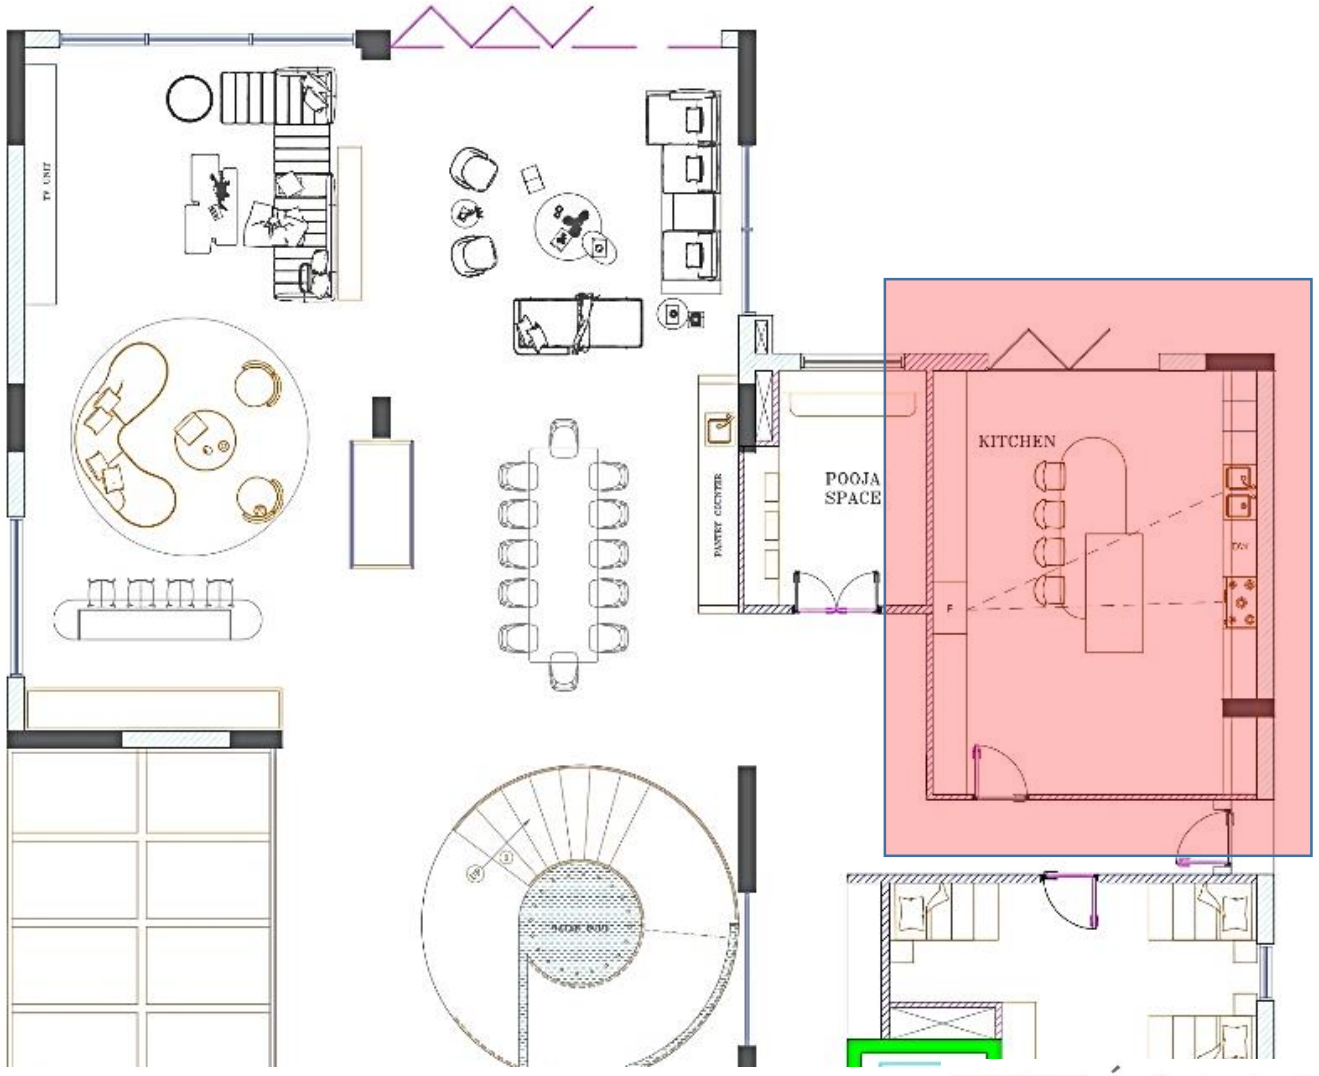


KITCHEN

éCLAT CONCEPT DESIGN

Working towards Perfection .....




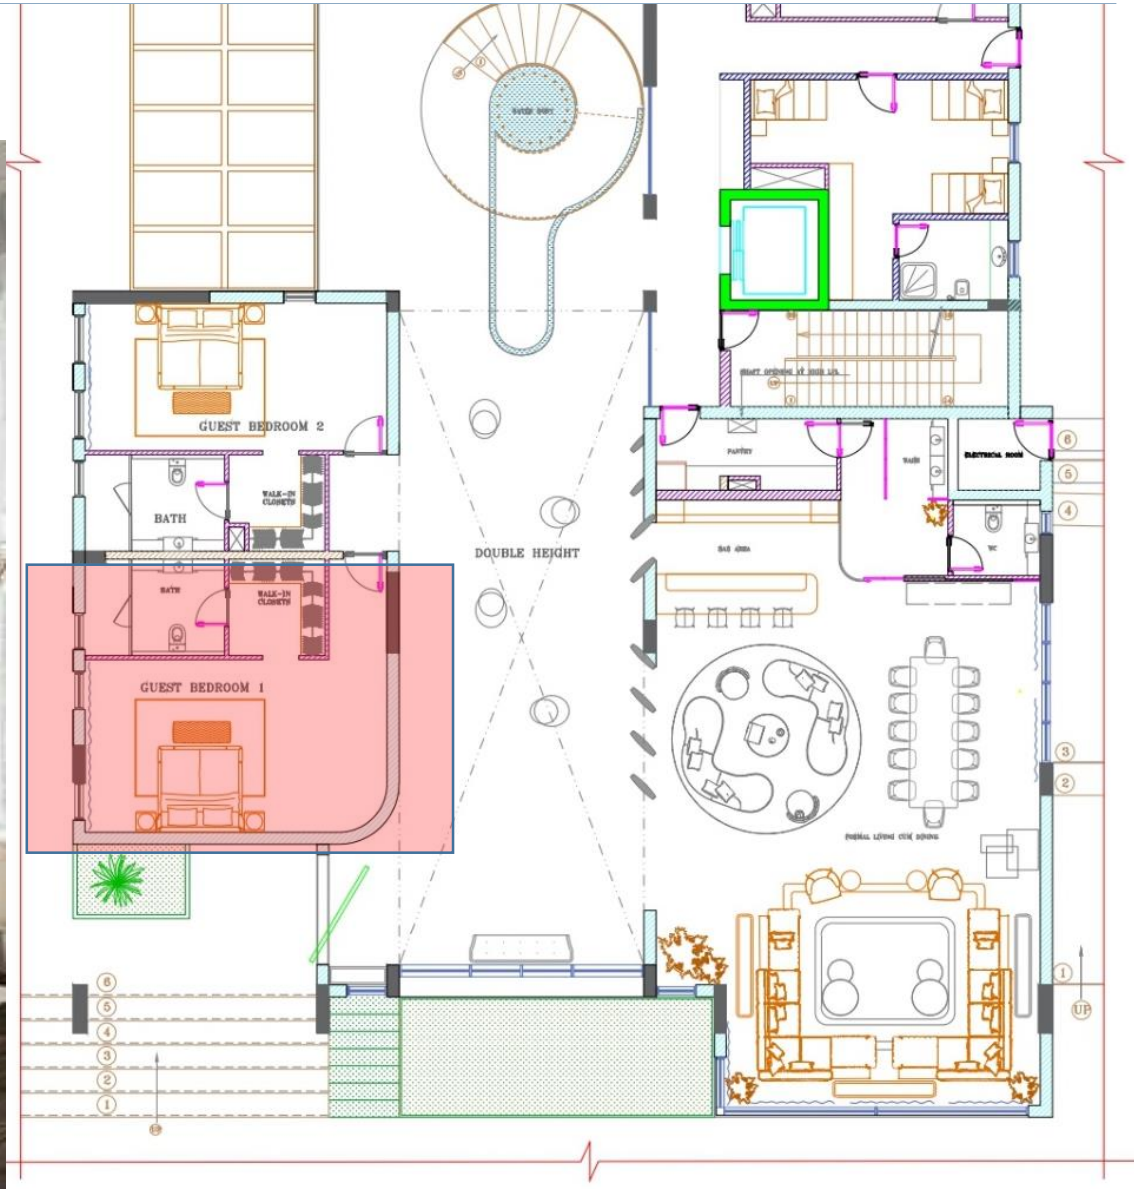

GUEST BEDROOM 01

éCLAT CONCEPT DESIGN
Working towards Perfection .....




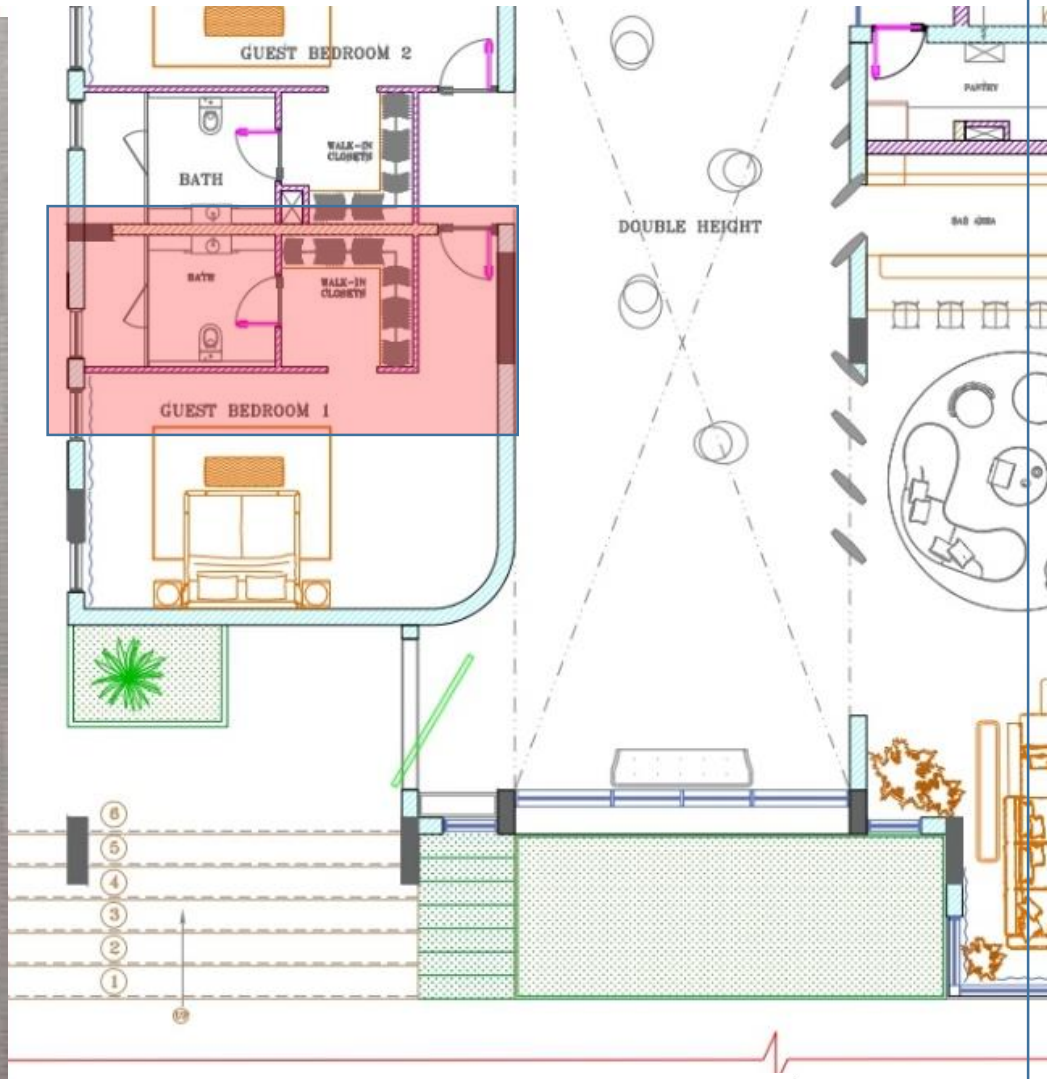

GUEST BEDROOM 01
WALK IN CLOSET

éCLAT CONCEPT DESIGN
Working towards Perfection .....



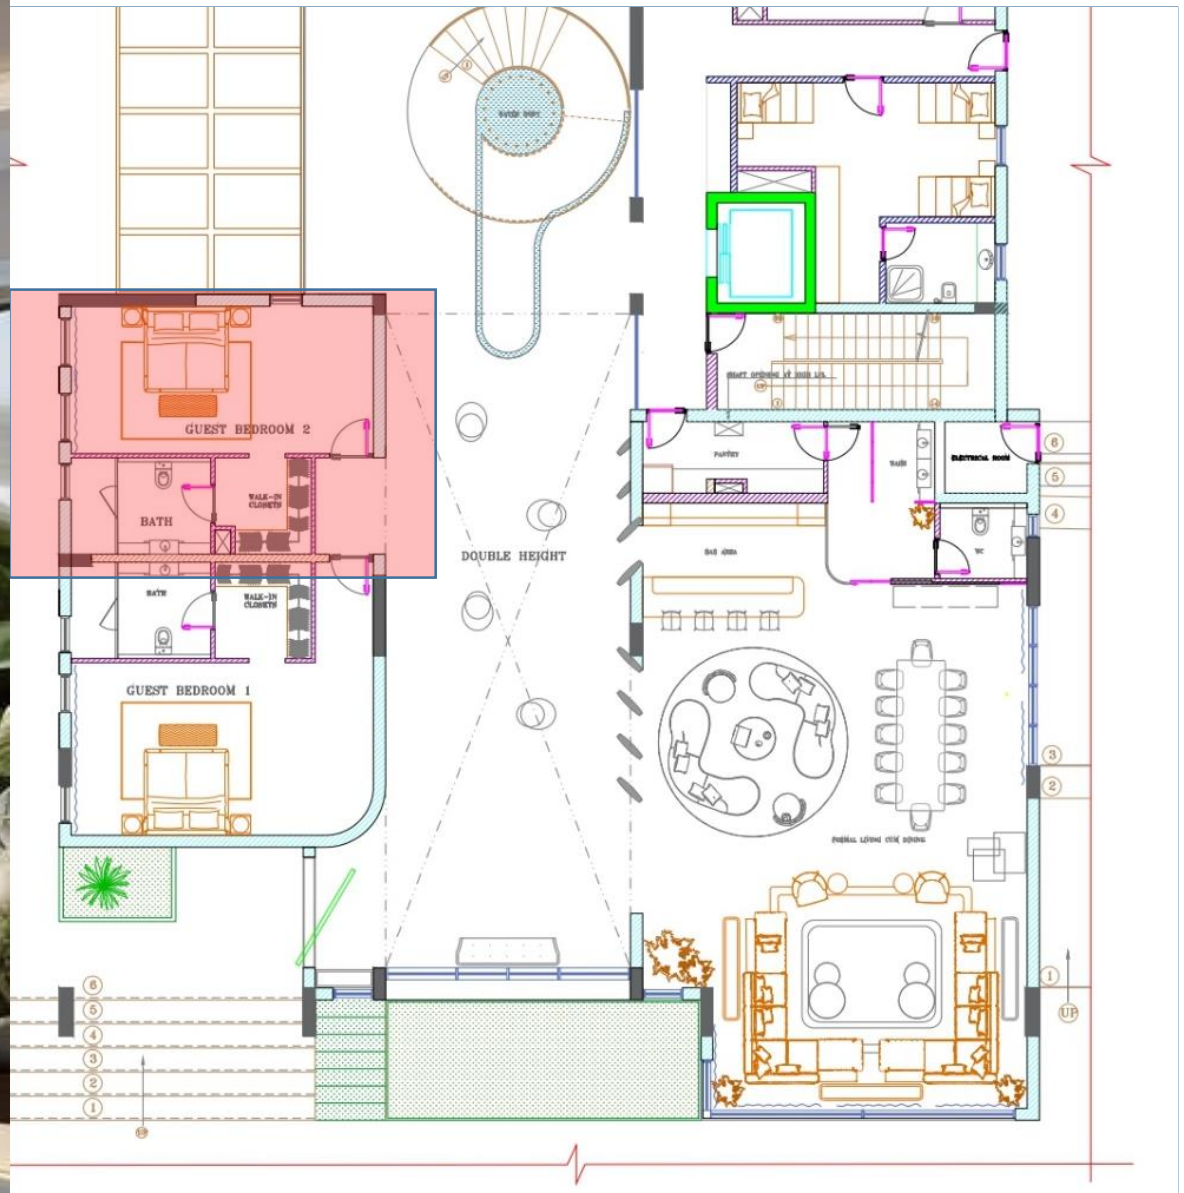


GUEST BEDROOM 02

éCLAT CONCEPT DESIGN


Working towards Perfection .....



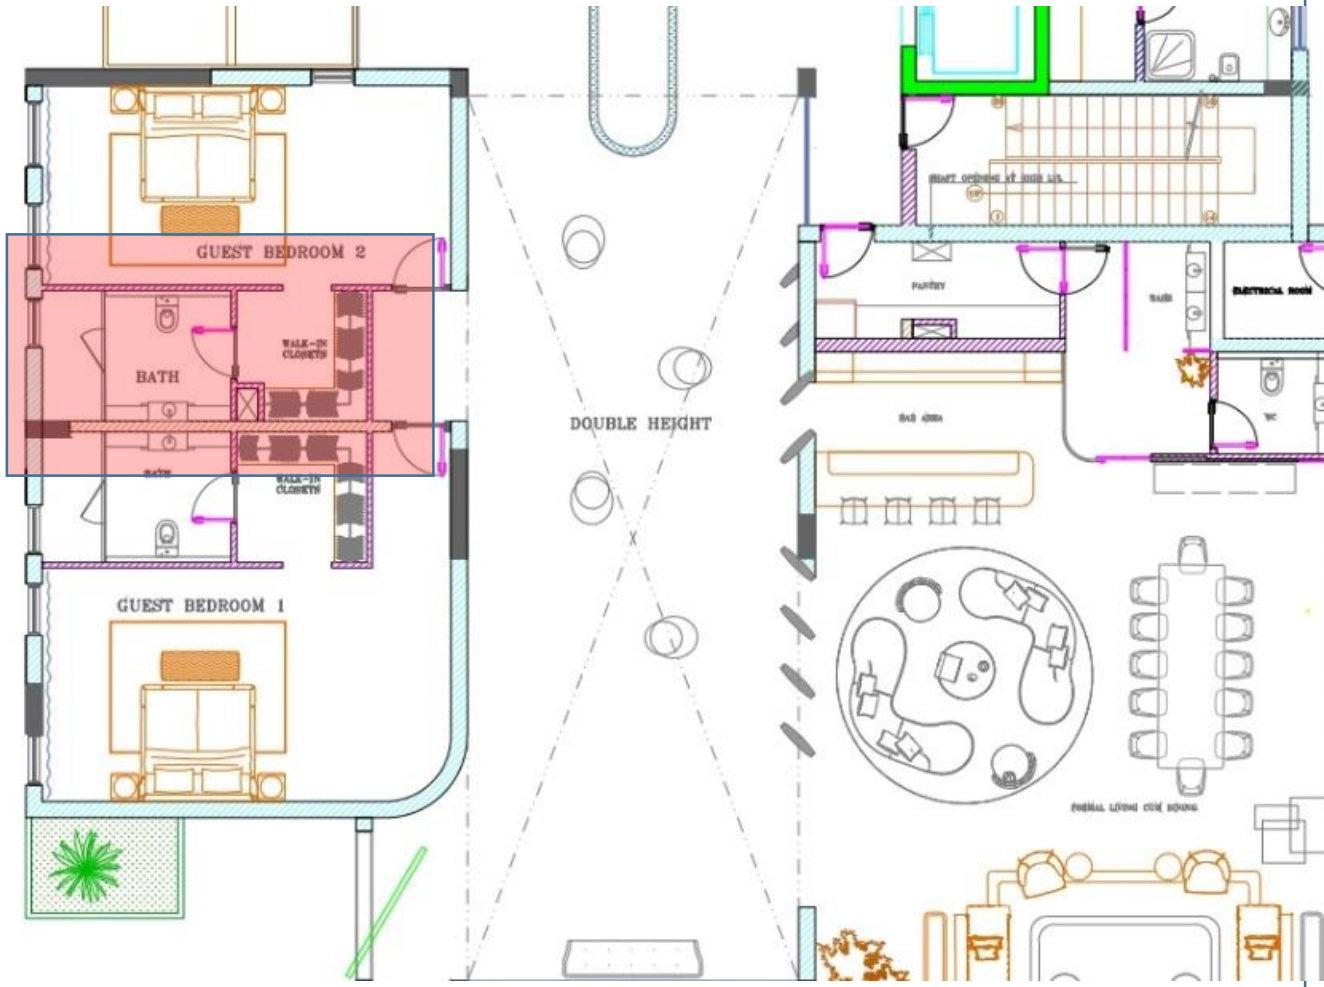

GUEST BEDROOM 02
WALK IN CLOSET


éCLAT CONCEPT DESIGN
Working towards Perfection .....

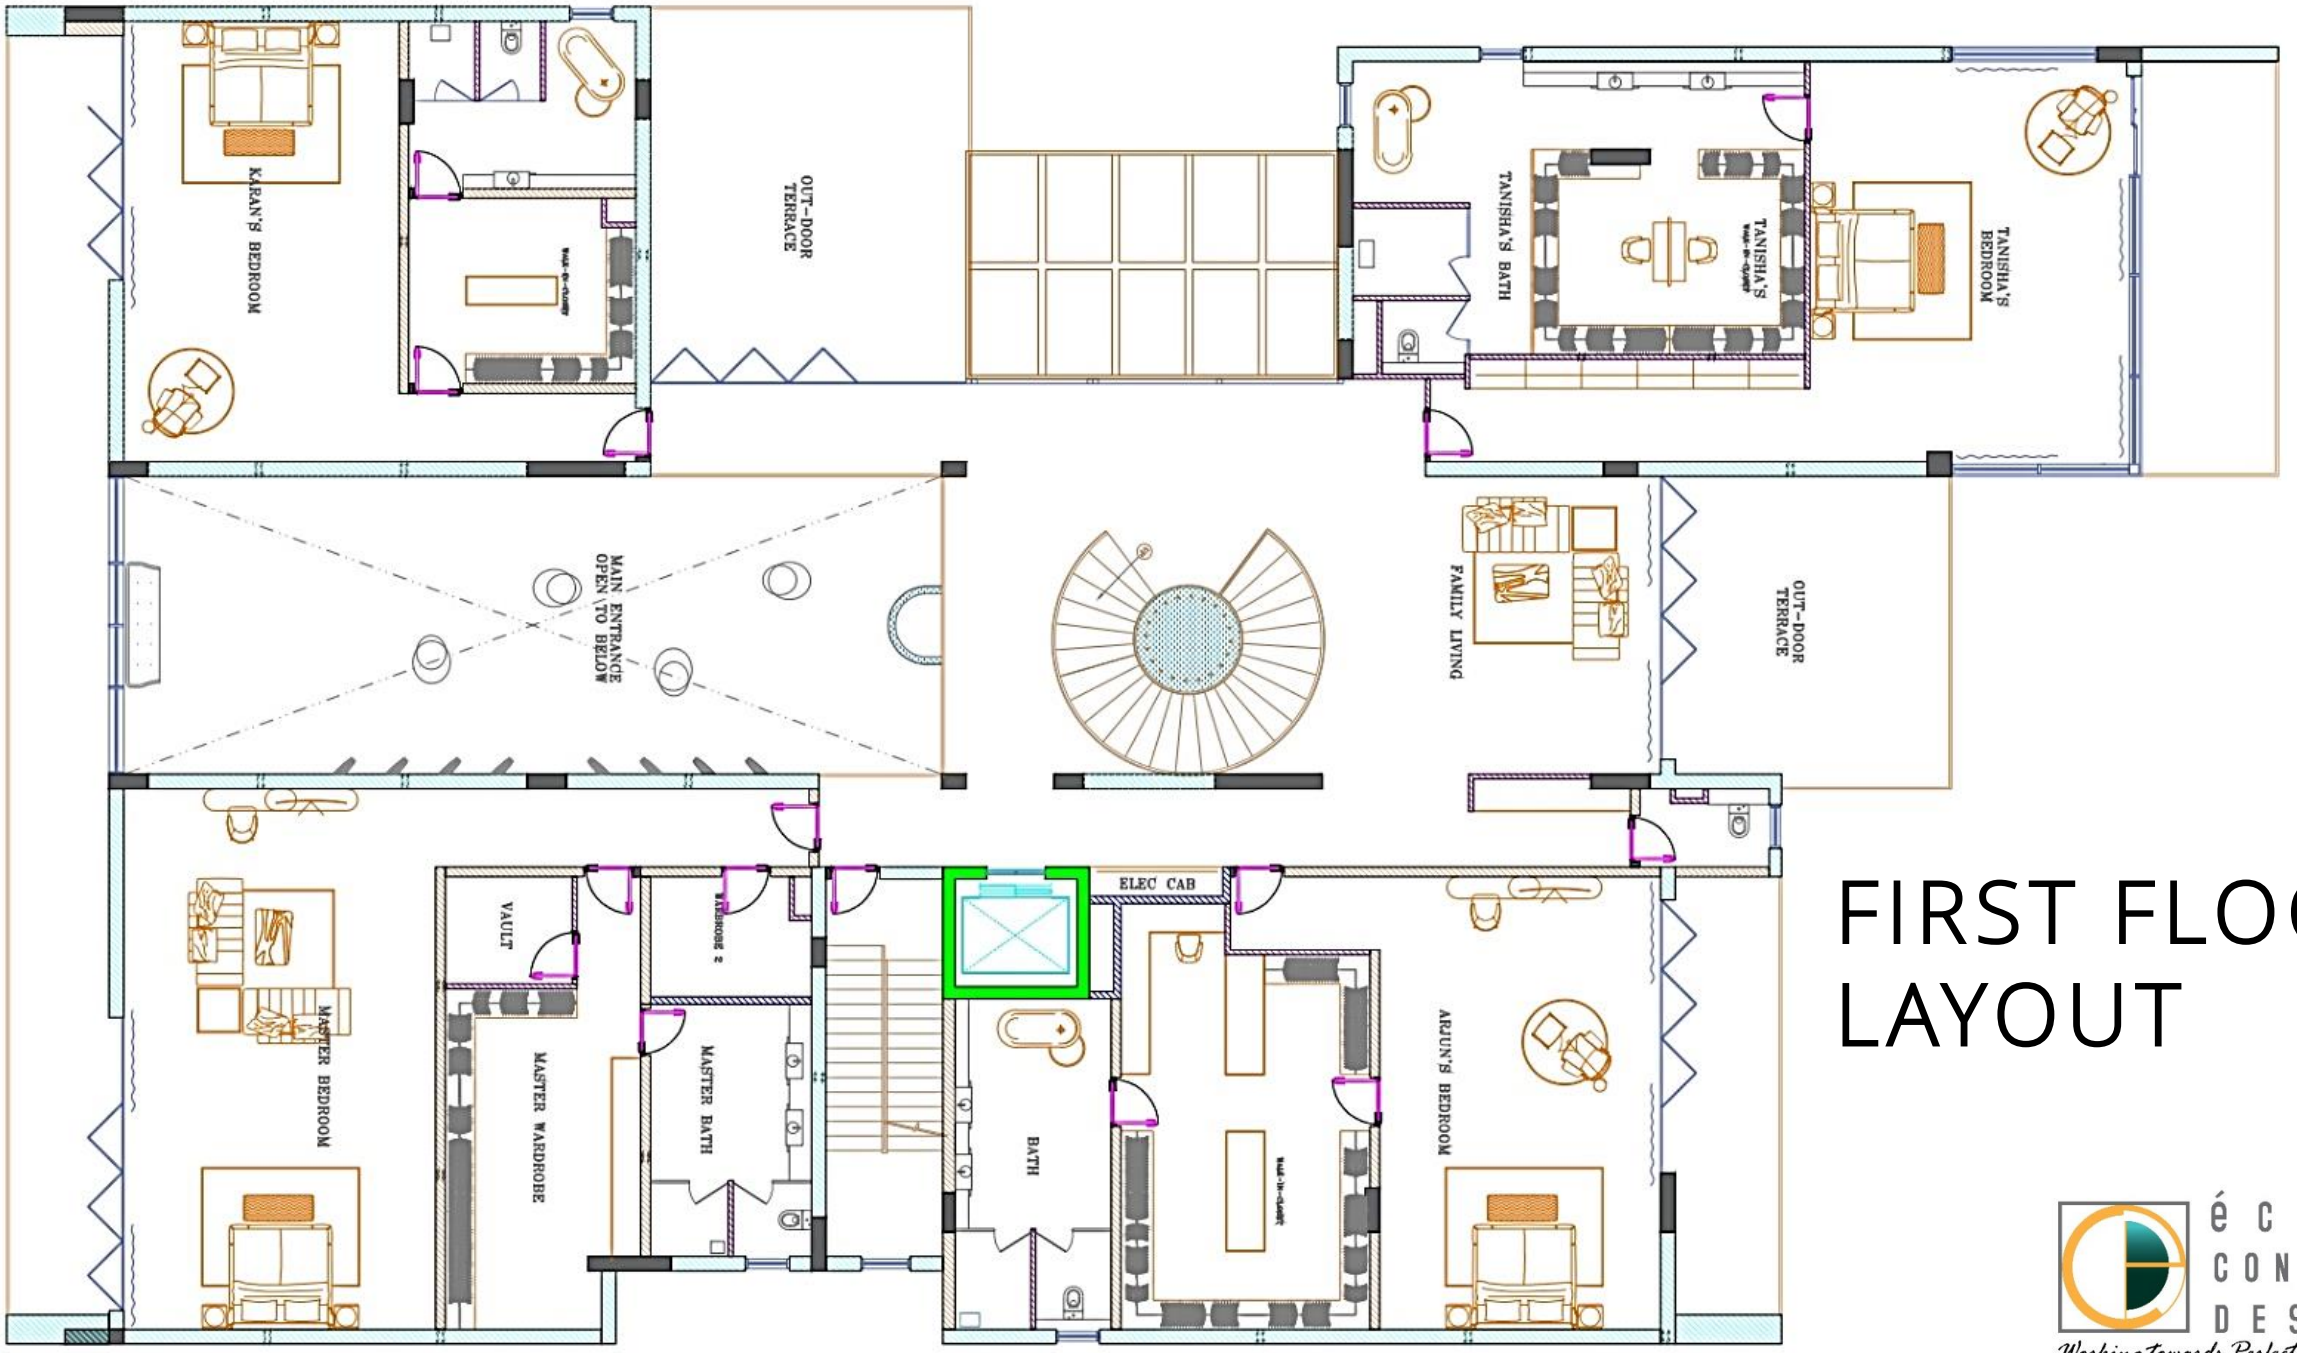

FIRST FLOOR LAYOUT

éCLAT CONCEPT DESIGN
Working towards Perfection .....



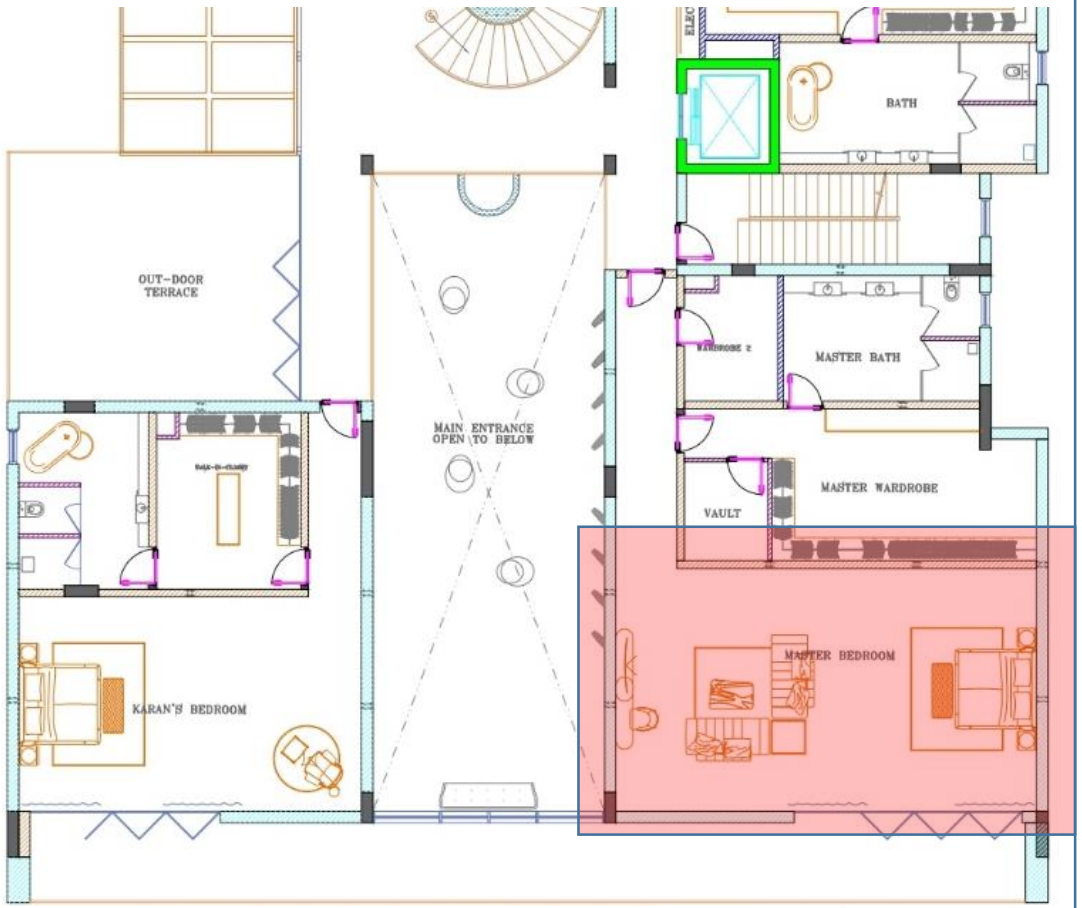


MASTER BED ROOM

éCLAT CONCEPT DESIGN

Working towards Perfection .....




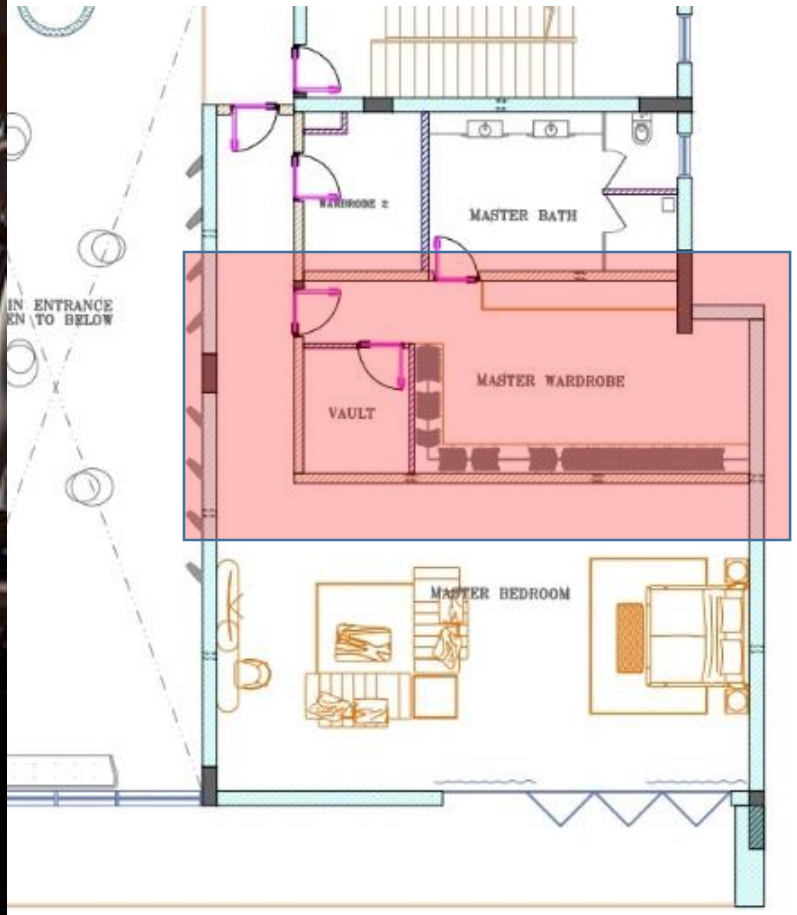

FF MASTER WALK IN CLOSET

éCLAT CONCEPT DESIGN
Working towards Perfection .....




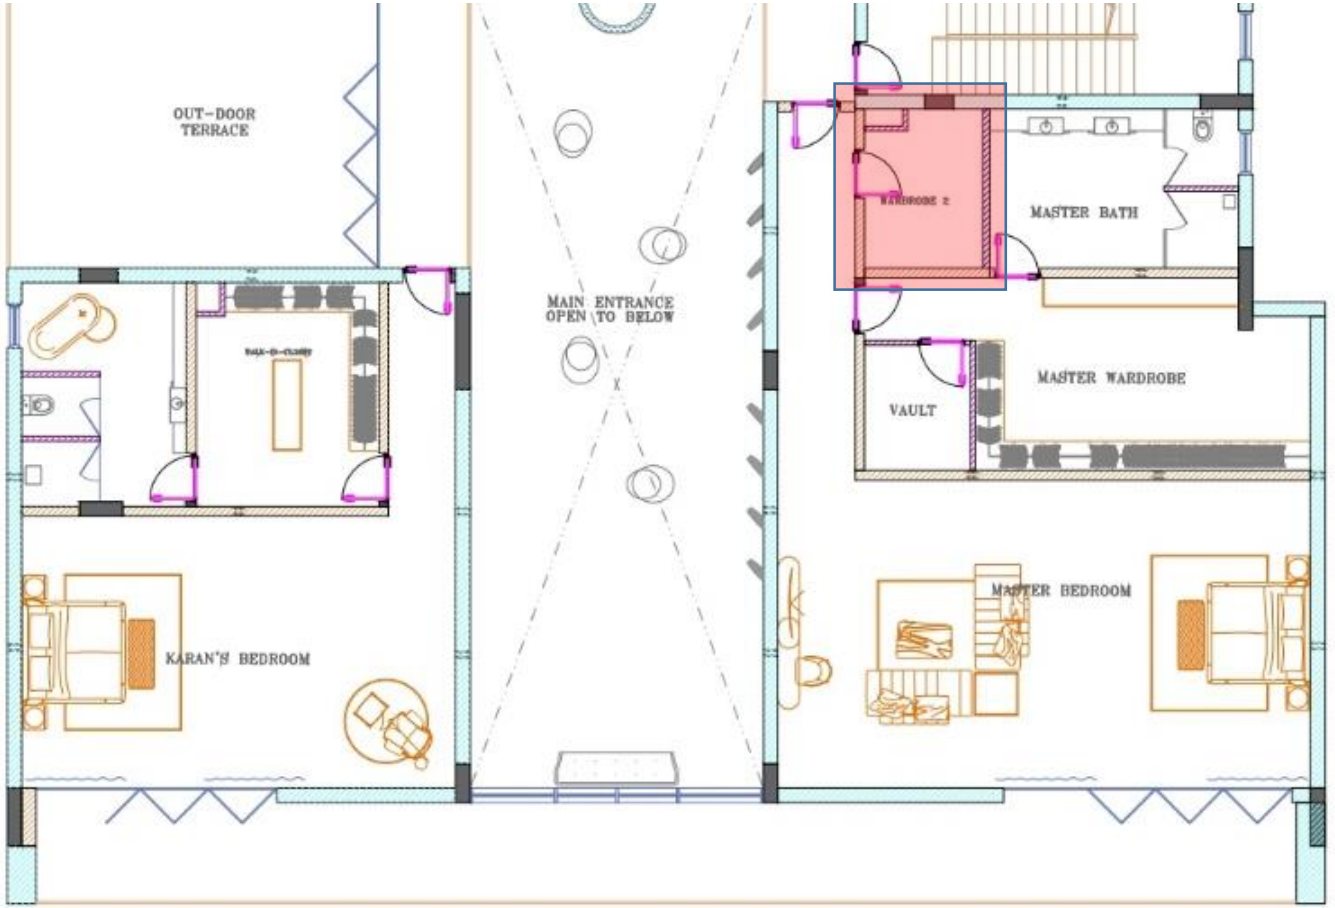

FF MASTER WALK IN CLOSET 02

éCLAT
CONCEPT
DESIGN
Working towards Perfection .....



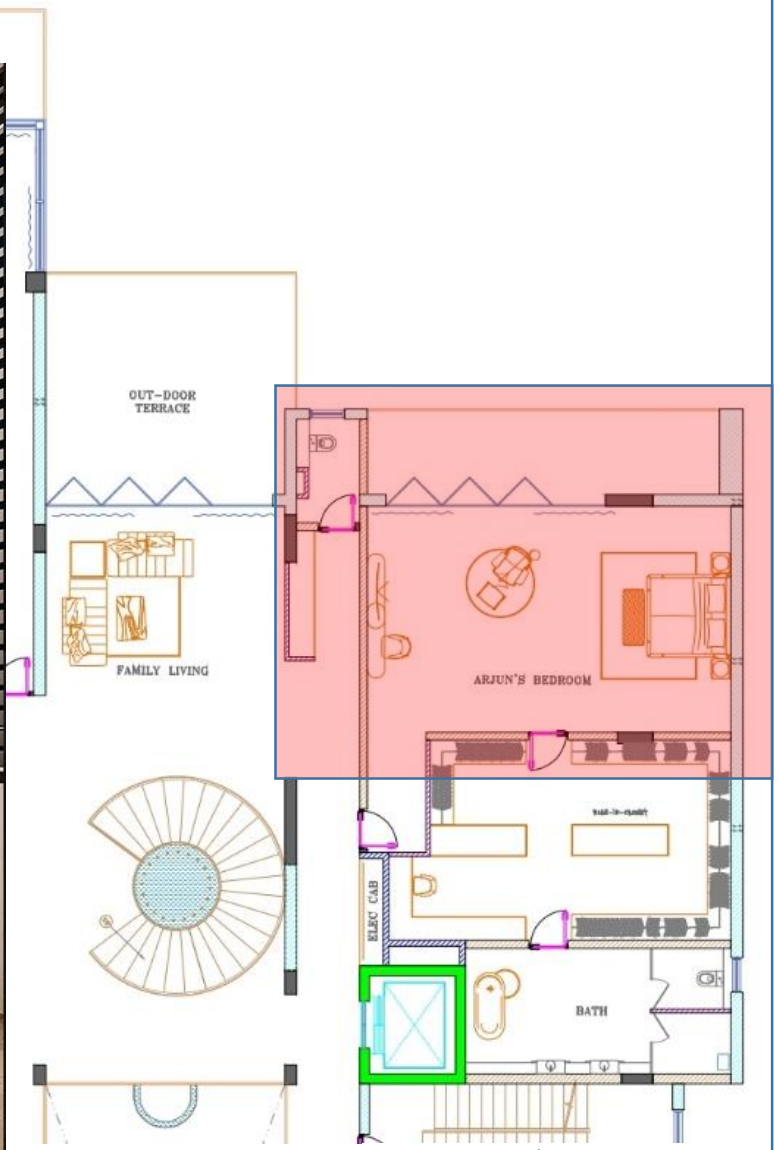


FF ARJUN'S BEDROOM

éCLAT CONCEPT DESIGN

Working towards Perfection .....




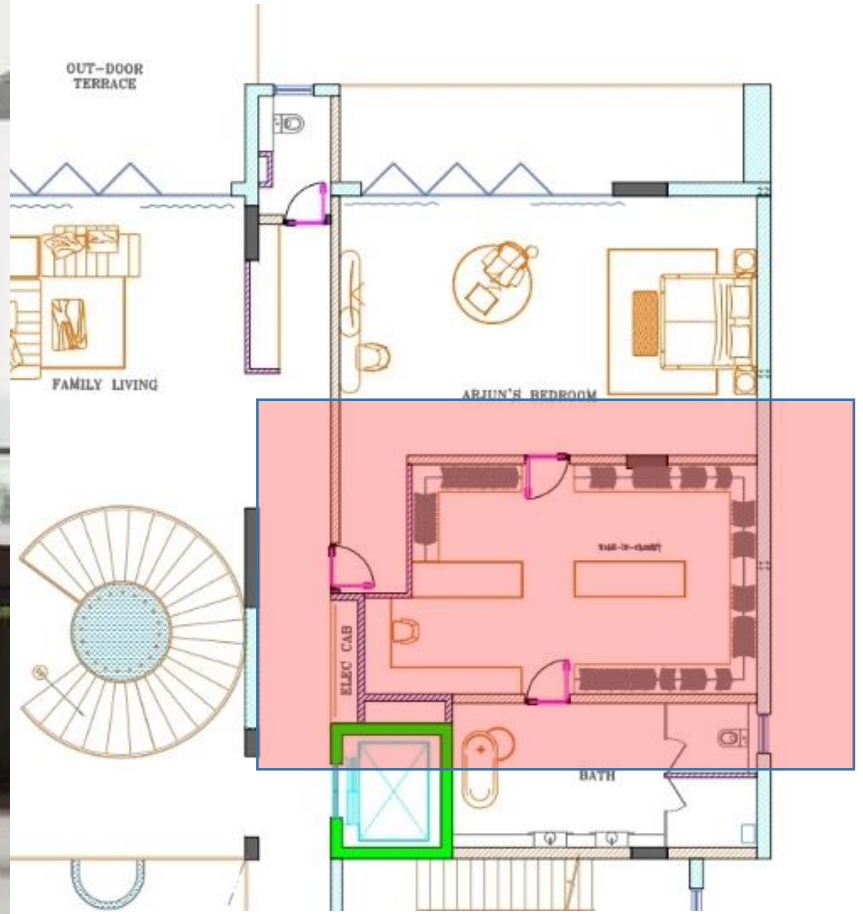

FF ARJUN'S WALK IN CLOSET

éCLAT CONCEPT DESIGN
Working towards Perfection .....




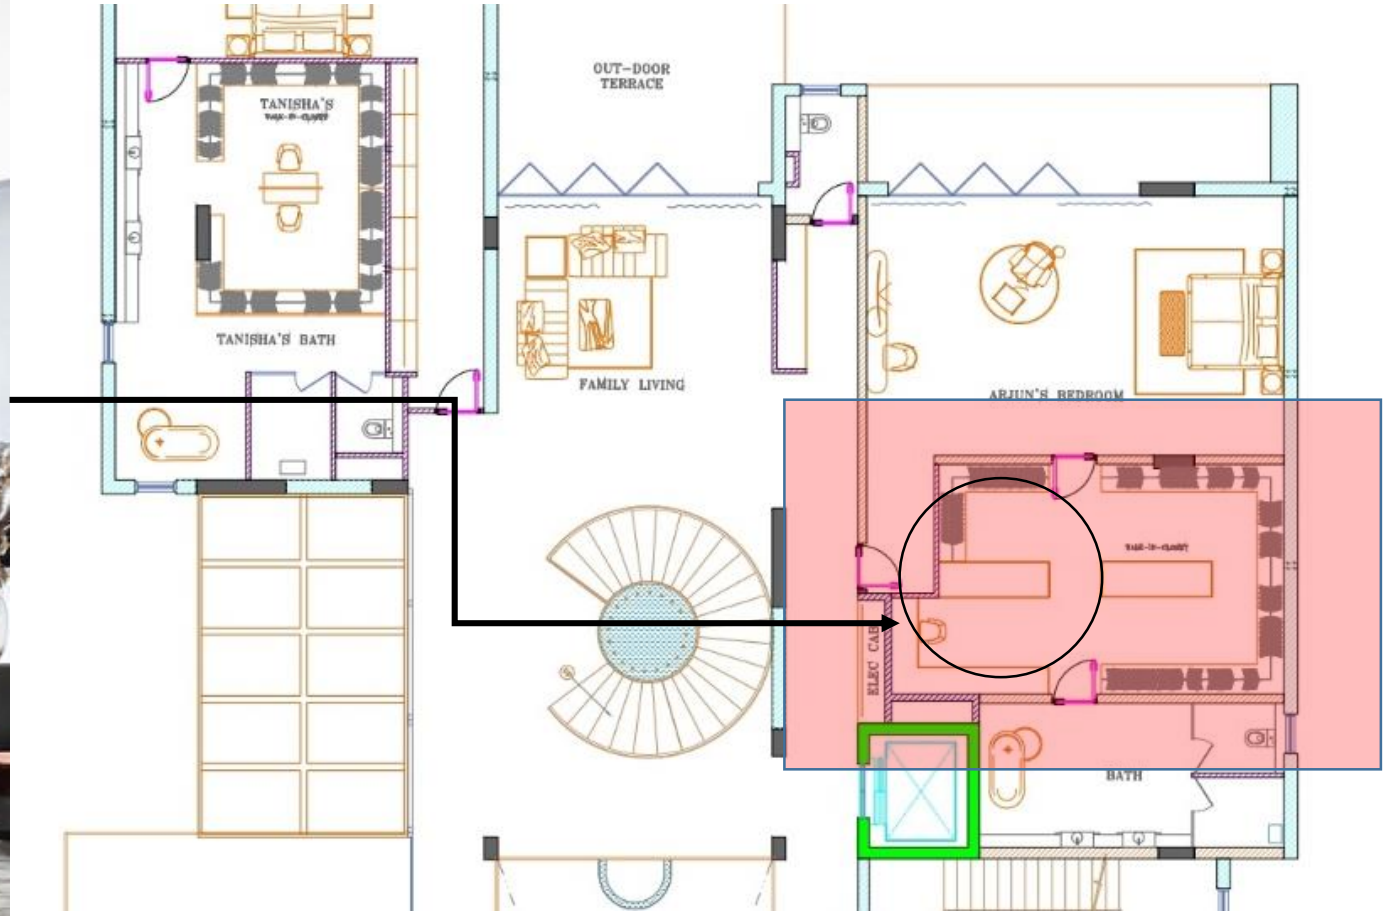

FF ARJUN'S WALK IN CLOSET

éCLAT CONCEPT DESIGN
Working towards Perfection .....



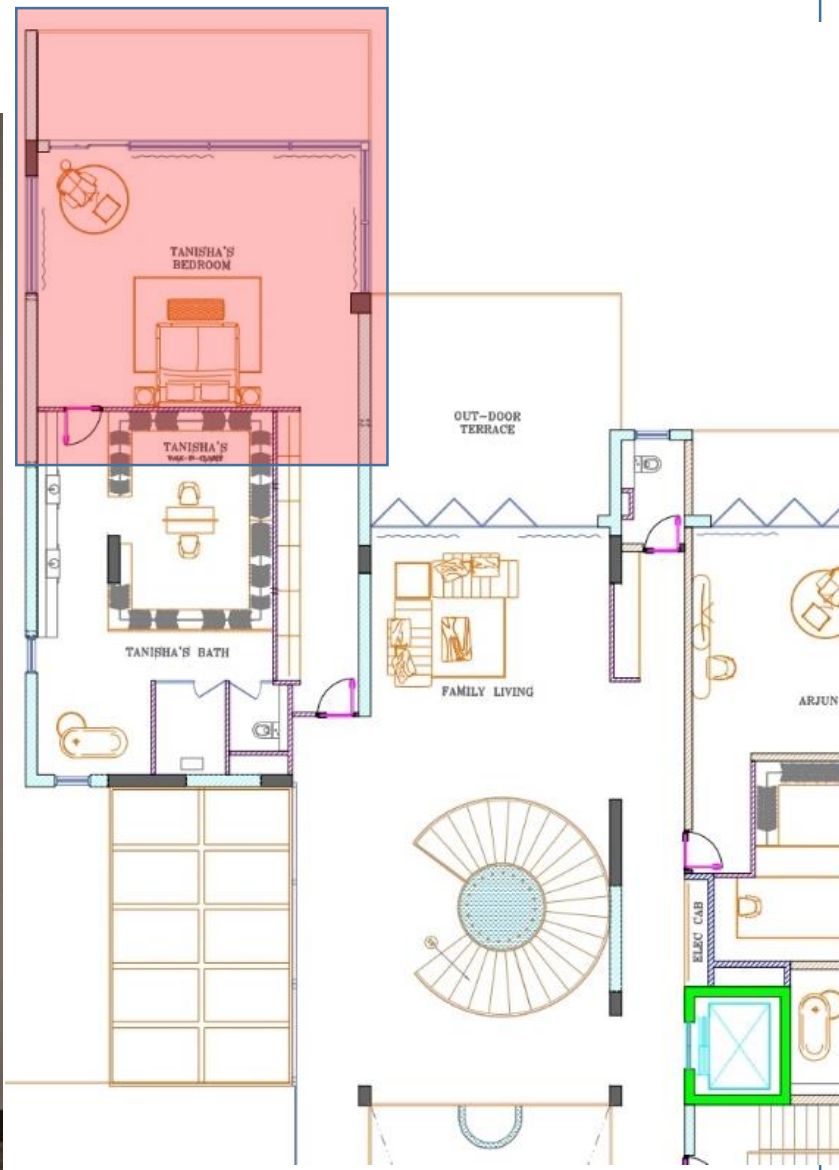


FF TANISHA'S BEDROOM

éCLAT CONCEPT DESIGN

Working towards Perfection .....




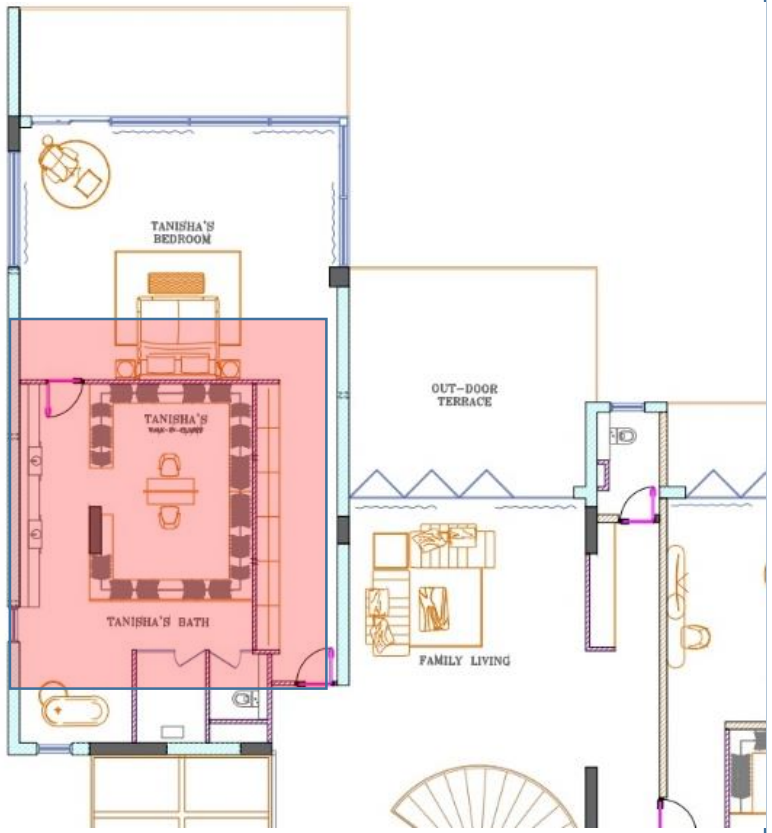

FF TANISHA'S WALK IN CLOSET

éCLAT CONCEPT DESIGN
Working towards Perfection .....



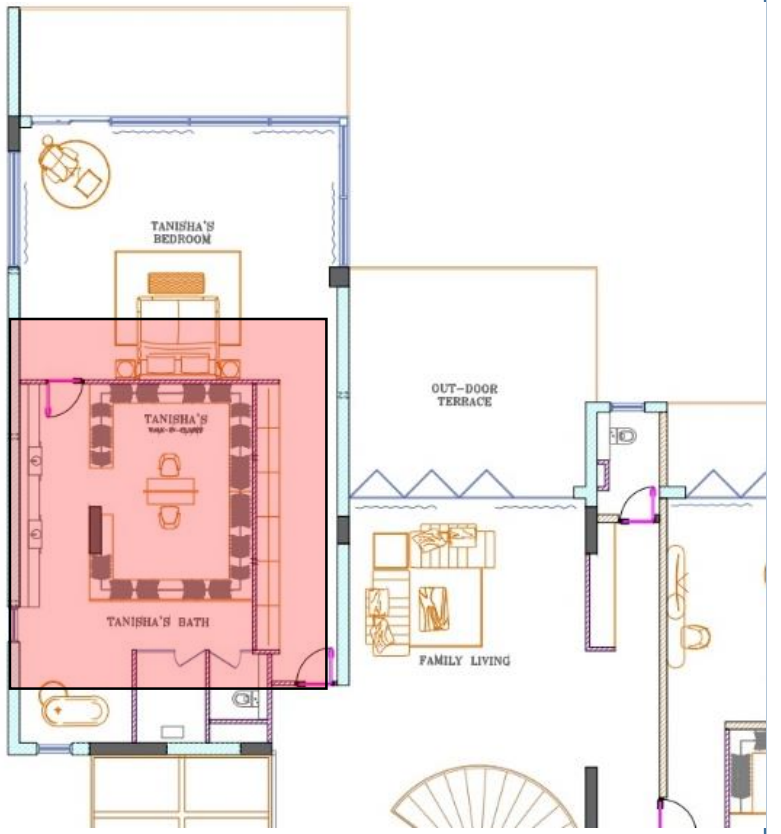


FF TANISHA'S WALK IN CLOSET

éCLAT CONCEPT DESIGN

Working towards Perfection .....



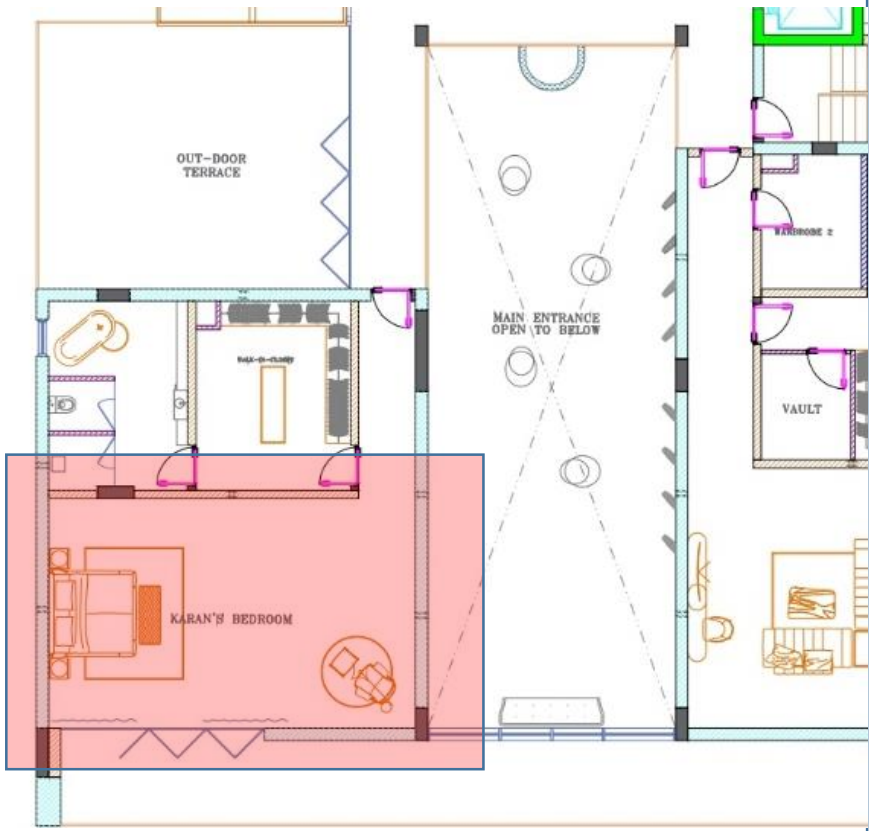


FF KARAN'S BEDROOM

éCLAT CONCEPT DESIGN

Working towards Perfection .....





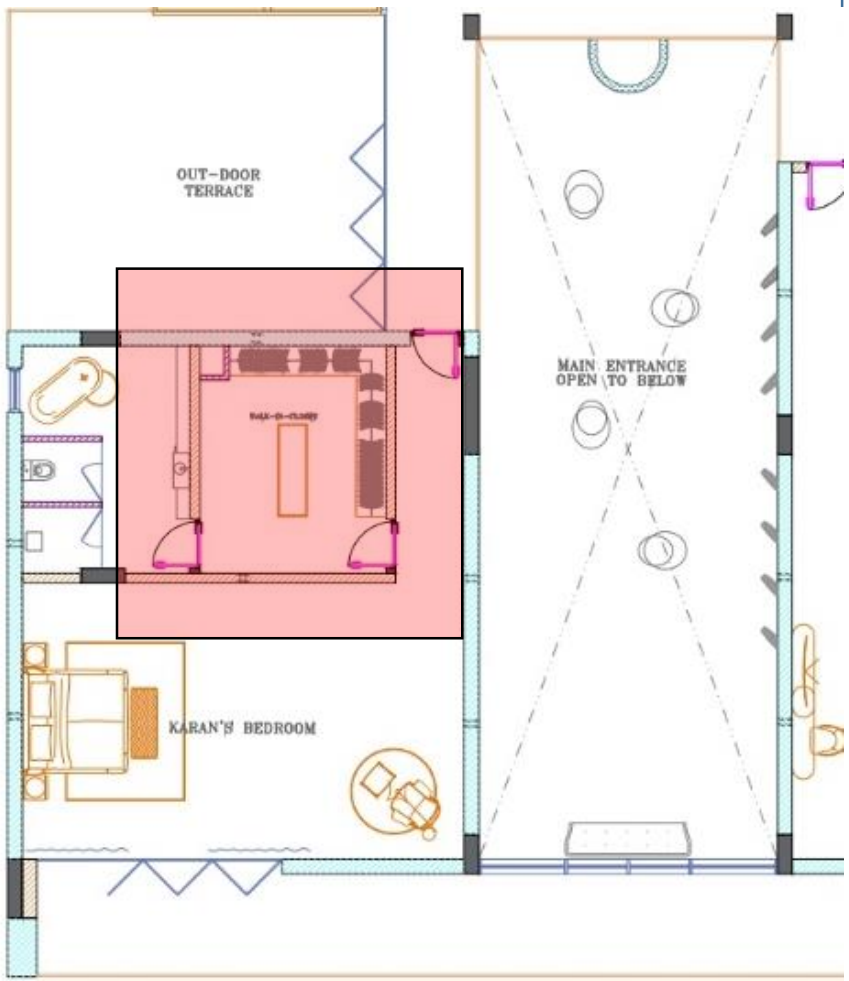

FF KARAN'S
WALK IN CLOSET

éCLAT
CONCEPT
DESIGN
Working towards Perfection .....

ROOF TOP LAYOUT

éCLAT CONCEPT DESIGN
Working towards Perfection .....





LANDSCAPE LAYOUT

éCLAT CONCEPT DESIGN
Working towards Perfection .....